FECHA: _____

HORA INICIO: _____

HORA FINAL: _____

REALIZADO POR: _____

RESPONSABLE TQ: _____

SACRIFICIO – PULIDO

Zona sucia · desde la mesa de camales (MPV-500) hasta la salida a zona limpia

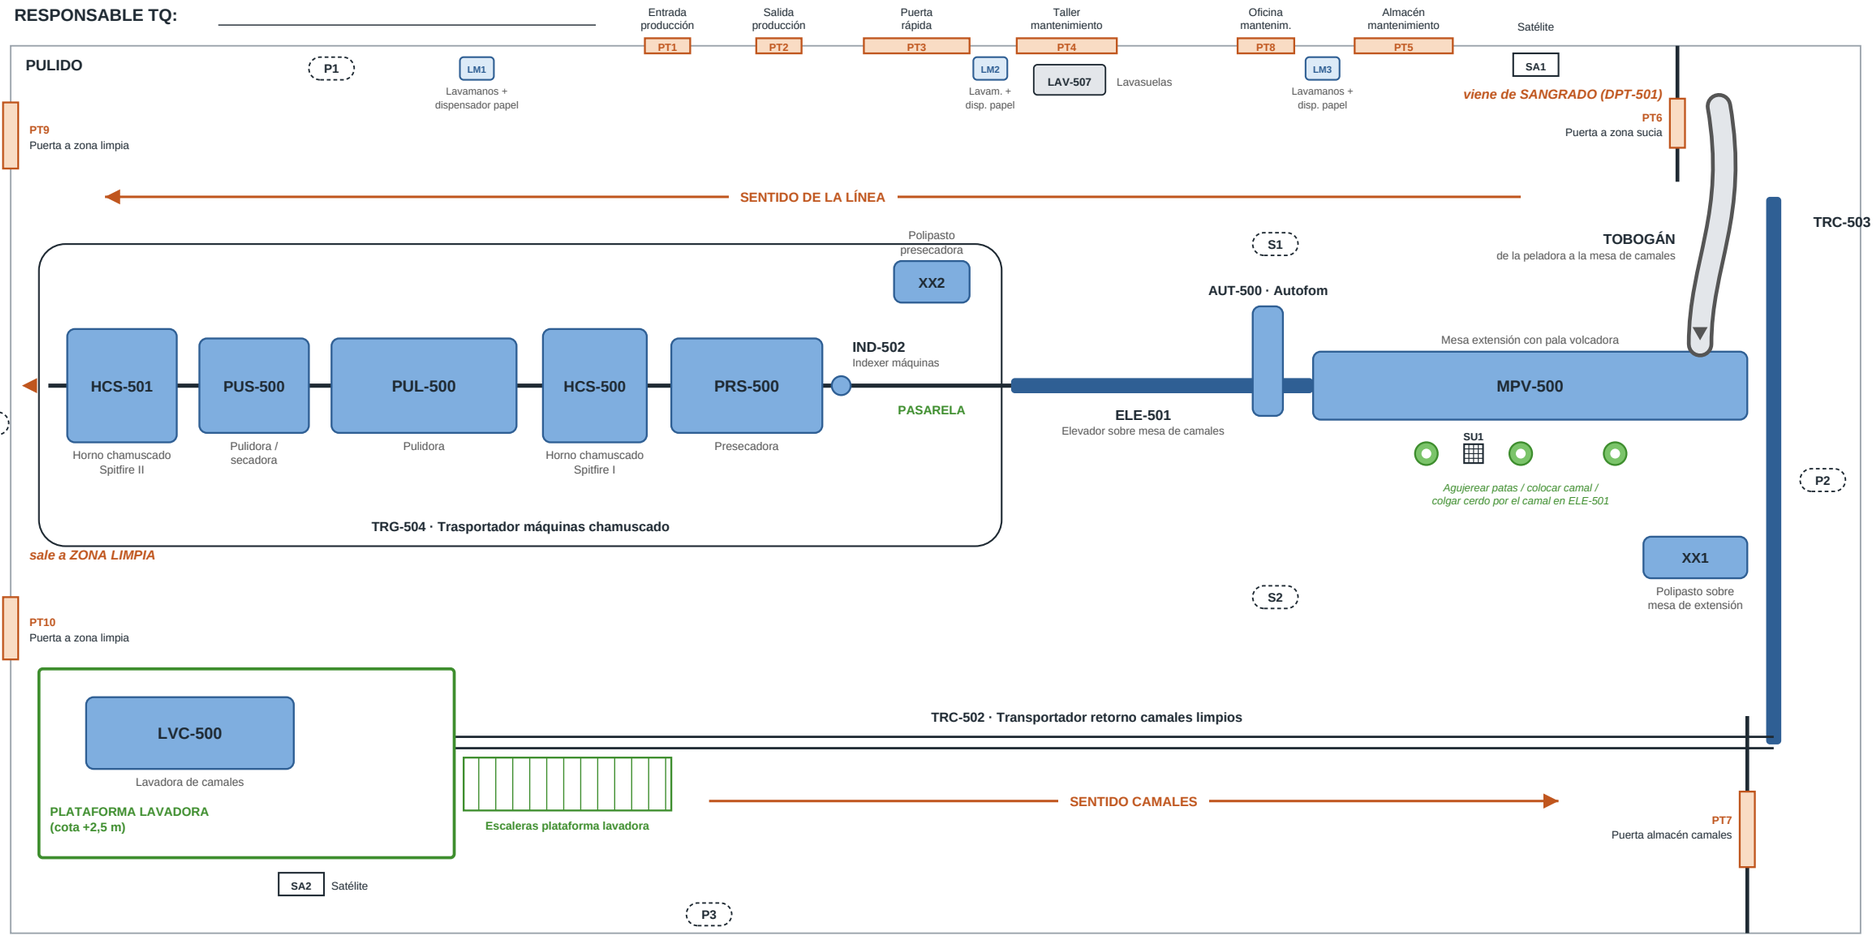

SALA SACRIFICIO – PULIDO

TOBOGÁN	De la peladora a la mesa de camales
MPV-500	Mesa extensión con pala volcadora
XX1	Polipasto sobre mesa de extensión
ELE-501	Elevador sobre mesa de camales
AUT-500	Autofom
TRC-503	Transp. retorno camales descenso
XX2	Polipasto presecadora
IND-502	Indexer máquinas
PRS-500	Presecadora
HCS-500	Horno chamuscado Spitfire I
PUL-500	Pulidora
PUS-500	Pulidora / secadora
HCS-501	Horno chamuscado Spitfire II
TRG-504	Trasportador máquinas chamuscado
TRC-502	Transp. retorno camales limpios
LVC-500	Lavadora de camales
LAV-507	Lavasuelas (vado taller mantenimiento)
SU1	Sumidero 1 (mesa de camales)
LM1	Lavamanos y dispensador papel (izq.)
LM2	Lavamanos y dispensador papel (pta. rápida)
LM3	Lavamanos y dispensador papel (oficina mant.)
SA1	Satélite (junto a zona sucia)
SA2	Satélite (plataforma lavadora)
ESCALERAS	Escaleras plataforma lavadora
PT1	Puerta entrada producción
PT2	Puerta salida producción
PT3	Puerta rápida
PT4	Puerta taller mantenimiento
PT5	Puerta almacén mantenimiento
PT6	Puerta a zona sucia
PT7	Puerta almacén camales
PT8	Puerta oficina mantenimiento
PT9	Puerta a zona limpia (arriba)
PT10	Puerta a zona limpia (abajo)
PASARELA	Pasarela (tramo de línea IND-502 a ELE-501)
S1	Suelo lado puertas (mesa camales)
S2	Suelo lado retorno camales
P1	Pared superior (puertas)
P2	Pared derecha (zona sucia / almacén)
P3	Pared inferior
P4	Pared izquierda (salida zona limpia)

Techos: pendientes de añadir.