FECHA: _____

HORA INICIO: _____

HORA FINAL: _____

REALIZADO POR: _____

RESPONSABLE TQ: _____

SACRIFICIO – SANGRADO

Zona sucia · desde el restrainer hasta las depiladoras

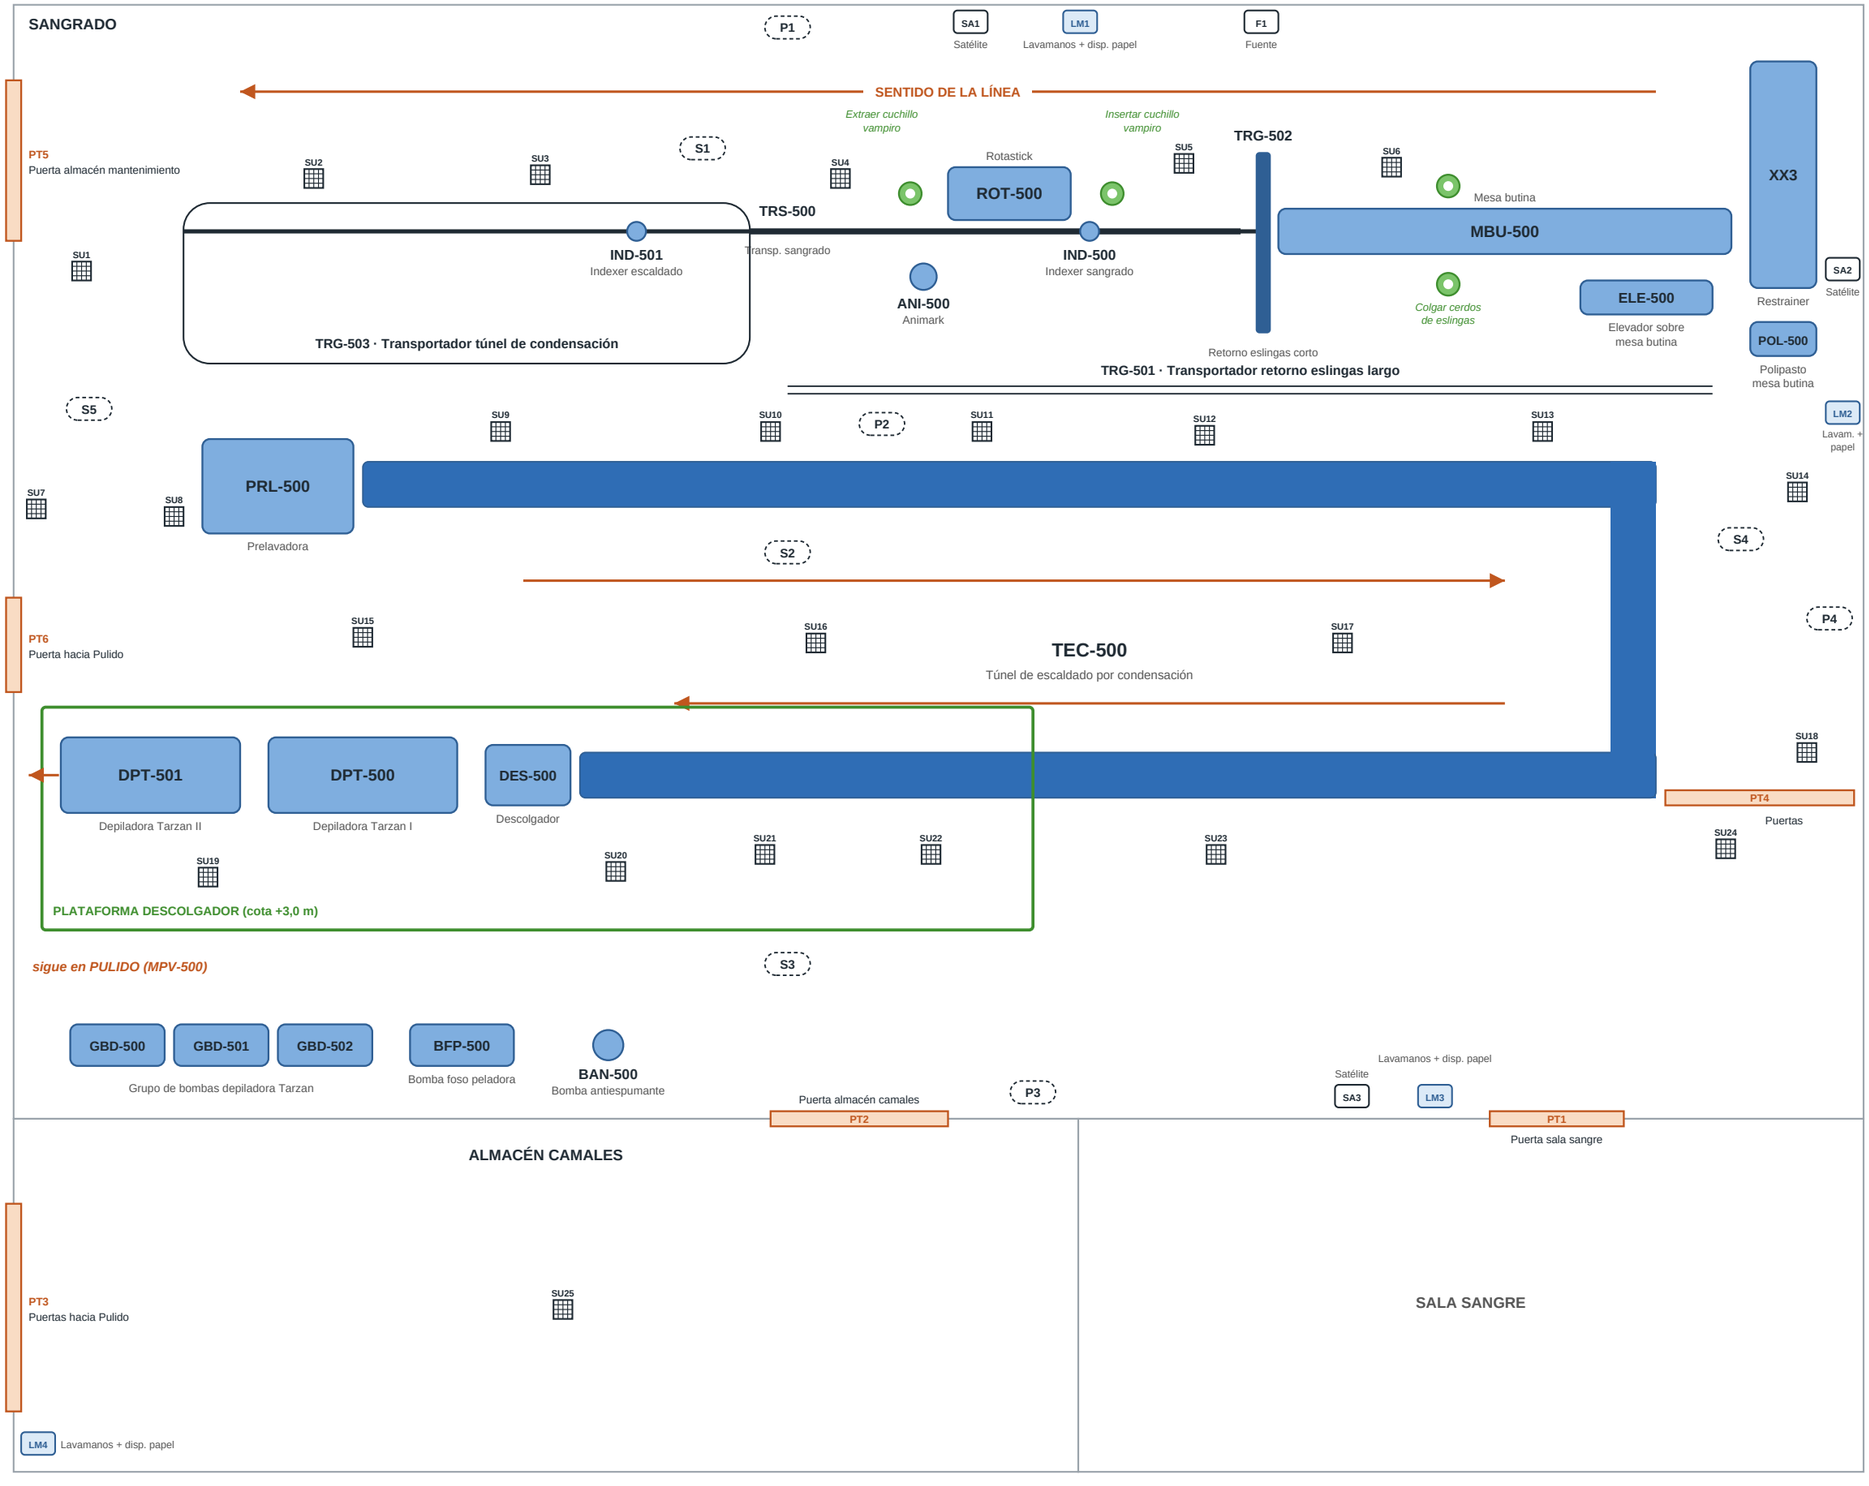

SALA SACRIFICIO – SANGRADO

XX3	Restrainer
MBU-500	Mesa butina
POL-500	Polipasto mesa butina
ELE-500	Elevador sobre mesa butina
TRG-502	Transp. retorno eslingas corto
TRG-501	Transp. retorno eslingas largo
IND-500	Indexer sangrado
ROT-500	Rotastick
ANI-500	Animark
TRS-500	Transportador sangrado
IND-501	Indexer escaldado
TRG-503	Transp. túnel de condensación
PRL-500	Prelavadora
TEC-500	Túnel escaldado por condensación
DES-500	Descolgador
DPT-500	Depiladora Tarzan I
DPT-501	Depiladora Tarzan II
GBD-500	Grupo bombas depiladora
GBD-501	Grupo bombas depiladora
GBD-502	Grupo bombas depiladora
BFP-500	Bomba foso peladora
BAN-500	Bomba antiespumante
PT1	Puerta sala sangre
PT2	Puerta almacén camales
PT3	Puertas hacia Pulido (almacén)
PT4	Puertas (entre TEC-500 y pared dcha.)
PT5	Puerta almacén mantenimiento
PT6	Puerta hacia Pulido (pared izq.)
LM1	Lavamanos + disp. papel (arriba)
LM2	Lavamanos + disp. papel (dcha.)
LM3	Lavamanos + disp. papel (abajo)
LM4	Lavamanos + disp. papel (almacén)
SA1	Satélite (arriba)
SA2	Satélite (dcha.)
SA3	Satélite (abajo)
F1	Fuente
S1	Suelo zona de arriba (sangrado)
S2	Suelo dentro del túnel (U)
S3	Suelo zona de abajo (bombas)
S4	Suelo lado derecho del túnel
S5	Suelo lado izquierdo (prelavadora)
P1	Pared de arriba
P2	Pared junto al túnel (TEC-500)
P3	Pared de abajo
P4	Pared derecha

SU1	Sumidero 1
SU2	Sumidero 2
SU3	Sumidero 3
SU4	Sumidero 4
SU5	Sumidero 5
SU6	Sumidero 6
SU7	Sumidero 7
SU8	Sumidero 8
SU9	Sumidero 9
SU10	Sumidero 10
SU11	Sumidero 11
SU12	Sumidero 12
SU13	Sumidero 13
SU14	Sumidero 14
SU15	Sumidero 15
SU16	Sumidero 16
SU17	Sumidero 17
SU18	Sumidero 18
SU19	Sumidero 19
SU20	Sumidero 20
SU21	Sumidero 21
SU22	Sumidero 22
SU23	Sumidero 23
SU24	Sumidero 24
SU25	Sumidero 25 (almacén camales)

Techos: pendientes.